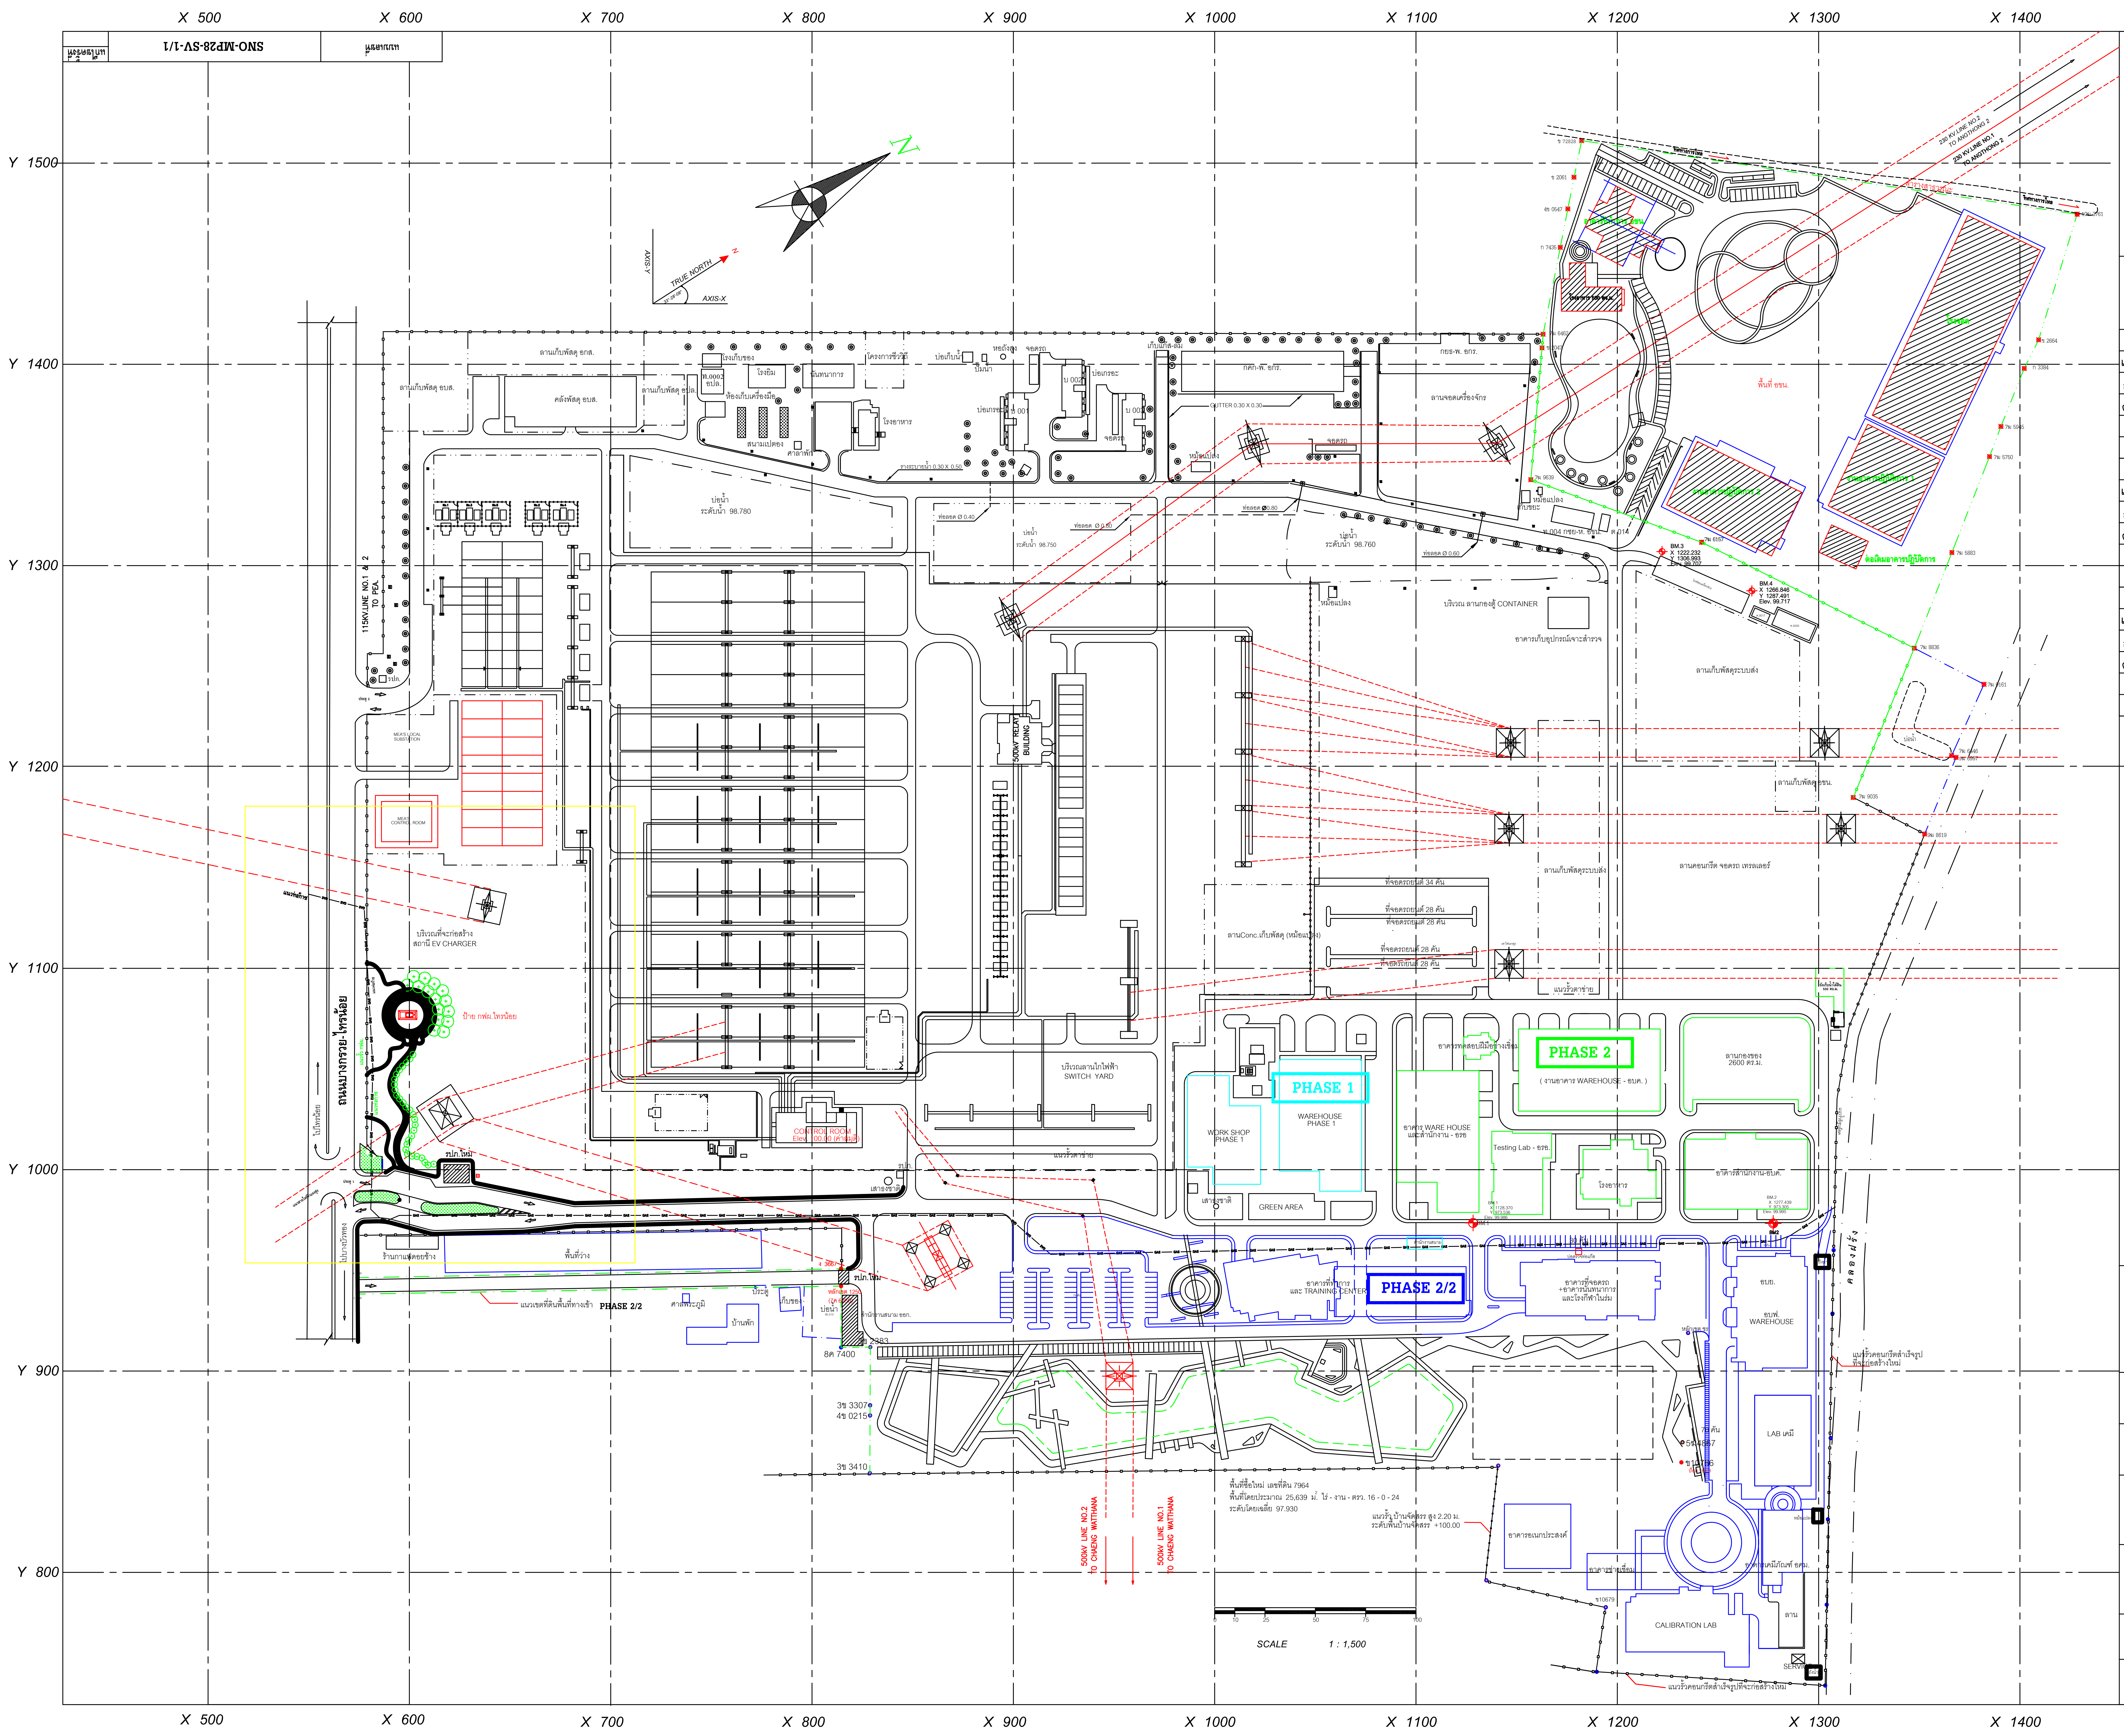
X 500
X 600
X 700
X 800
X 900
X 1000
X 1100
X 1200
X 1300
X 1400
Y 1500
Y 1400
Y 1300
Y 1200
Y 1100
Y 1000
Y 900
Y 800
แบบเลขที่
SNO-MP28-SV-1/1
N
TRUE NORTH
AXIS-X
AXIS-Y
115KV LINE NO.1 & 2 TO PEA
ถนนบางกรวย-ไทรน้อย
ป้าย กฟผ.ไทรน้อย
บริเวณที่จะก่อสร้าง สถานี EV CHARGER
500kV RELAY BUILDING
บริเวณลานไกไฟฟ้า SWITCH YARD
CONTROL ROOM
ลานConc.เก็บพัสดุ (หม้อแปลง)
ที่จอดรถยนต์ 28 คัน
ที่จอดรถยนต์ 34 คัน
แนวรั้วตาข่าย
บริเวณ ลานกองตู้ CONTAINER
ลานเก็บพัสดุระบบส่ง
PHASE 1
WAREHOUSE PHASE 1
WORK SHOP PHASE 1
เสาธงชาติ
GREEN AREA
อาคาร WARE HOUSE และสำนักงาน - อรอ
อาคารทดสอบฝีมือช่างเชื่อม
Testing Lab - อรอ.
โรงอาหาร
PHASE 2
(งานอาคาร WAREHOUSE - อบค.)
ลานกองของ 2600 ตร.ม.
อาคารสำนักงาน-อบค.
BM.1 X 1128.370 Y 973.536 Elev. 99.986
BM.2 X 1277.439 Y 973.305 Elev. 99.995
อาคารที่ทำการ และ TRAINING CENTER
PHASE 2/2
อาคารที่จอดรถ +อาคารนันทนาการ และโรงกีฬาในร่ม
บ่อตรวจท่อแก๊ส
อบย.
อบฟ. WAREHOUSE
LAB เคมี
CALIBRATION LAB
คลองฝั่ง
PHASE 2/2
500kV LINE NO.2 TO CHAENG WATTHANA
500kV LINE NO.1 TO CHAENG WATTHANA
พื้นที่ซื้อใหม่ เลขที่ดิน 7964
พื้นที่โดยประมาณ 25,639 ม.2 ไร่ - งาน - ตรว. 16 - 0 - 24
ระดับโดยเฉลี่ย 97.930
แนวรั้ว บ้านจัดสรร สูง 2.20 ม.
ระดับพื้นบ้านจัดสรร +100.00
อาคารอเนกประสงค์
อาคารช่างเชื่อม
ข10679
0 10 25 50 75 100
SCALE 1 : 1,500
230 KV LINE NO.1 TO ANGTHONG 2
230 KV LINE NO.2 TO ANGTHONG 2
Y 1500
Y 1400
Y 1300
Y 1200
Y 1100
Y 1000
Y 900
Y 800

การไฟฟ้าฝ่ายผลิตแห่งประเทศไทย
ฝ่ายออกแบบและบริหารงานก่อสร้าง
ได้รับการรับรอง ISO 9001:2008
53 หมู่ 2 ถนนจรัญสนิทวงศ์ บางกรวย นนทบุรี 11130 โทร 02-436-1910-3

งานออกแบบ และ เอกสารประกอบแบบถือเป็นสมบัติของ ฝ่ายออกแบบและบริหารงานก่อสร้าง การไฟฟ้าฝ่ายผลิตแห่งประเทศไทย ห้ามผู้ใดนำไปใช้งาน ทำซ้ำ หรือดัดแปลง โดยไม่ได้รับอนุญาตเป็นลายลักษณ์อักษร จาก การไฟฟ้าฝ่ายผลิตแห่งประเทศไทย

ครั้งที่		รายการแก้ไข	
เขียนแบบ			
ออกแบบ			
ตรวจสอบ			
เสนอ		เห็นชอบ	
อนุมัติ		วันที่	
ครั้งที่			
เขียนแบบ			
ออกแบบ			
ตรวจสอบ			
เสนอ		เห็นชอบ	
อนุมัติ		วันที่	
ครั้งที่		รายการแก้ไข รายการแก้ไข	
เขียนแบบ			
ออกแบบ			
ตรวจสอบ			
เสนอ		เห็นชอบ	
อนุมัติ		วันที่	

สถาปนิกโครงการ ....

สถาปนิก ....

สถาปนิกภายใน ....

ภูมิสถาปนิก ....

วิศวกรโครงสร้าง ....

วิศวกรสุขาภิบาล ....

วิศวกรไฟฟ้า ....

วิศวกรเครื่องกล ....

เขียนแบบ นายวสันต์ นิ่มนวล

ตรวจสอบ

(นายวสันต์ นิ่มนวล)
หัวหน้าชุดสำรวจ

(นายยุทธพงศ์ จิตตวิริยะกุล)
หัวหน้าแผนกข้อมูลงานช่าง

เสนอพิจารณา

(นายทนงศักดิ์ ธนปูณยนันท์)
หัวหน้ากองงานจ้างเหมา

เห็นชอบ

(นางทัศนีย์นาถ พฤกษไพบูลย์)
ผู้ช่วยผู้อำนวยการฝ่ายออกแบบและบริหารงานก่อสร้าง(ก่อสร้าง)

อนุมัติ

(นายอุรเคนทร์ ไวยสุศรี)
ผู้อำนวยการฝ่ายออกแบบและบริหารงานก่อสร้าง

สำนักงาน กฟผ.ไทรน้อย

งานอาคารของหน่วย บำรุงรักษา และขนส่ง

แบบแสดง

แผนที่บริเวณ (MASTER PLAN)

เลขที่งาน	แบบเลขที่	
253128	SNO-MP28-SV-1/1	
วันที่	จำนวนแผ่น	แก้ไขครั้งที่
	01	